



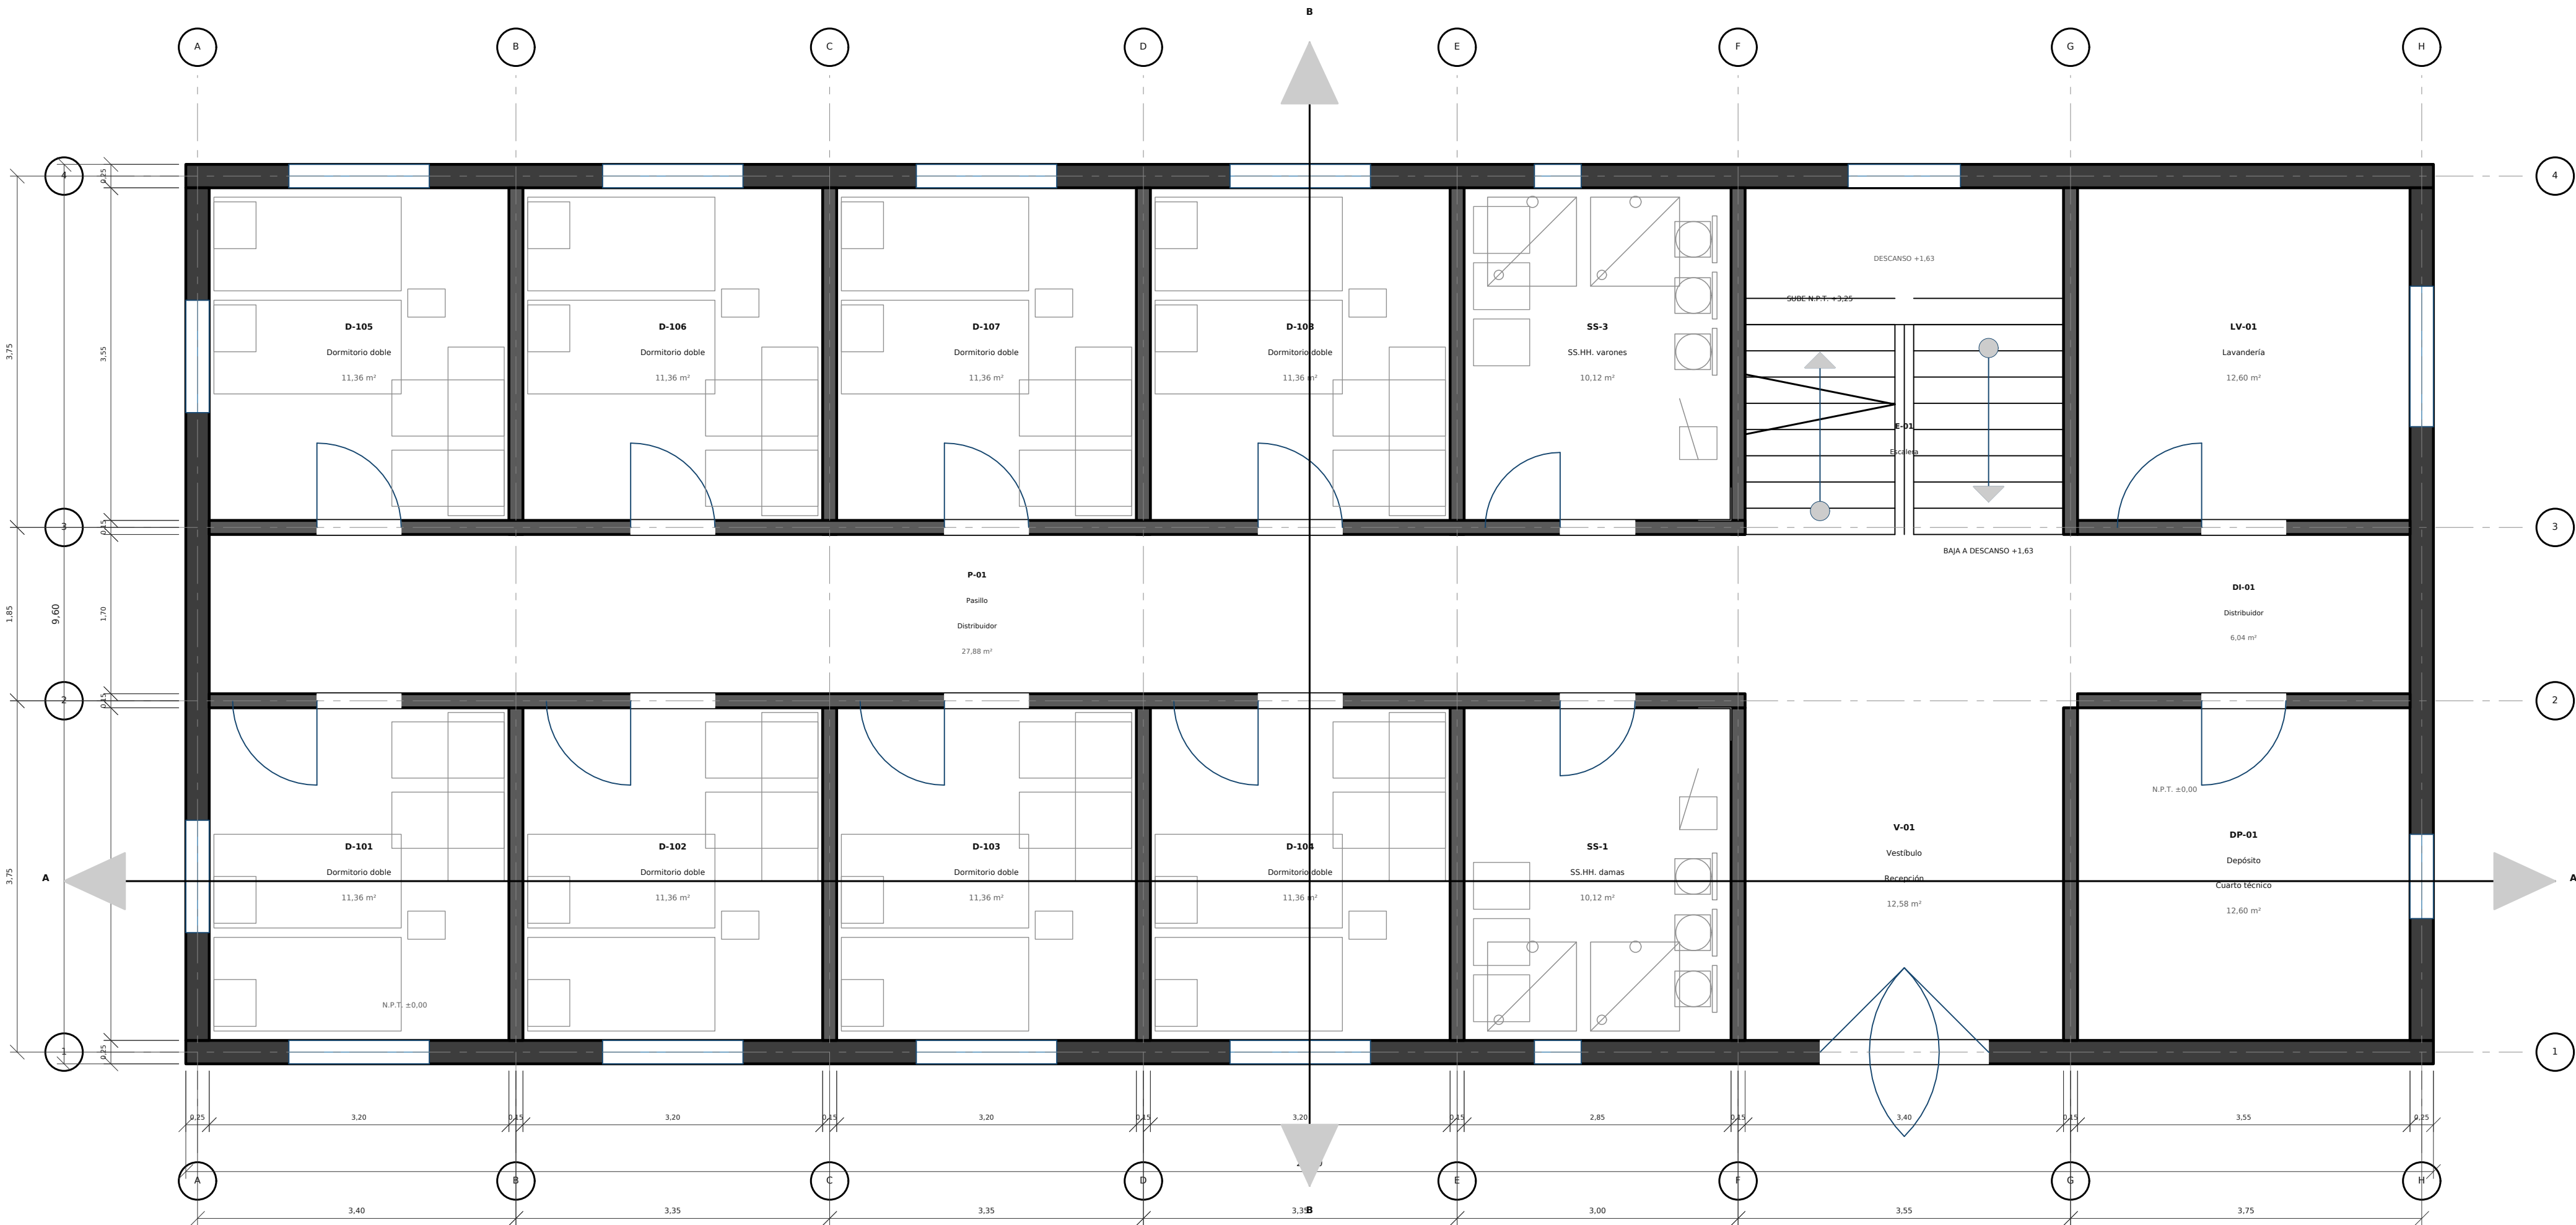

PLANTA BAJA · N.P.T. ±0,00
Escala 1:50 - cotes en metros - modificado tipo

SITUACIÓN · BLOQUE DORMITORIOS (D)

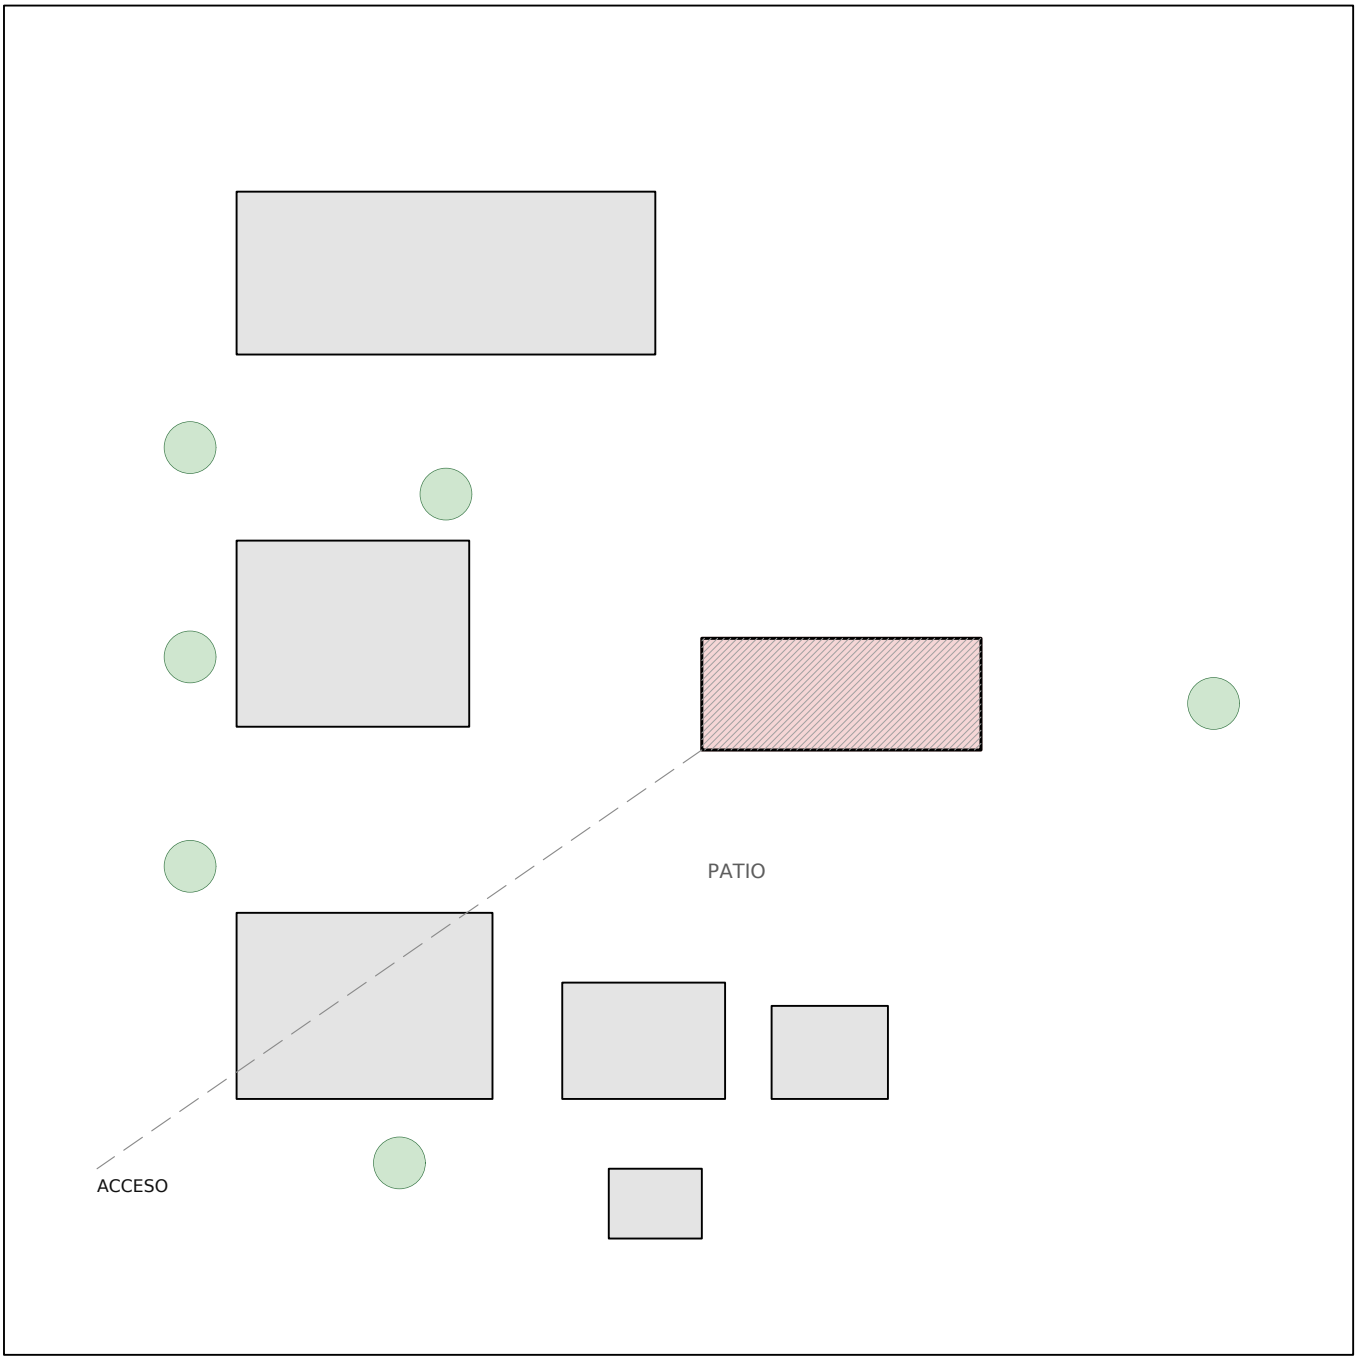

Escala 1:500 - predio de 100,00 x 100,00 m

Nivel	Cód.	Recinto	Área (m²)
P. BAJA	D-101	Dormitorio doble	11,36
P. BAJA	D-102	Dormitorio doble	11,36
P. BAJA	D-103	Dormitorio doble	11,36
P. BAJA	D-104	Dormitorio doble	11,36
P. BAJA	D-105	Dormitorio doble	11,36
P. BAJA	D-106	Dormitorio doble	11,36
P. BAJA	D-107	Dormitorio doble	11,36
P. BAJA	D-108	Dormitorio doble	11,36
P. BAJA	P-01	Paseo / Distribuidor	27,88
P. BAJA	SS-1	SS.HH. damas	10,12
P. BAJA	SS-3	SS.HH. varones	10,12
P. BAJA	LV-01	Lavandería	12,60
P. BAJA	DI-01	Deposito / Cuarto técnico	6,04
P. BAJA	DP-01	Deposito	12,60

Eje	X (m)	Entre ejes	Eje	Y (m)	Entre ejes
A	0,12	—	1	0,12	—
B	3,32	3,20	2	3,68	3,75
C	6,88	3,35	3	5,72	1,85
D	10,22	3,35	4	9,47	3,75
E	13,57	3,35			
F	16,92	3,00			
G	20,12	3,55			
H	23,88	3,75			

Nº	Tipo	Ubicación	Ancho	Alto	Abilizar	Cont.
V-101	Ventana 2 hojas	Fachada norte	1,50	1,50	+0,90	1
V-102	Ventana 2 hojas	Fachada norte	1,50	1,50	+0,90	1
V-103	Ventana 2 hojas	Fachada norte	1,50	1,50	+0,90	1
V-104	Ventana 2 hojas	Fachada norte	1,50	1,50	+0,90	1
V-201	Ventana 2 hojas	Fachada sur	1,50	1,50	+0,90	1
V-202	Ventana 2 hojas	Fachada sur	1,50	1,50	+0,90	1
V-203	Ventana 2 hojas	Fachada sur	1,50	1,50	+0,90	1
V-204	Ventana 2 hojas	Fachada sur	1,50	1,50	+0,90	1
V-31	Ventana alta	Fachada norte	0,50	0,80	+1,70	1
V-32	Ventana alta	Fachada sur	0,50	0,80	+1,70	1
V-41	Ventana	Fachada norte	1,20	0,95	+1,90	1
V-42	Ventana	Fachada este	0,90	1,00	+1,50	1
V-43	Ventana	Fachada este	1,50	1,20	+1,80	1
V-44	Ventana 2 hojas	Fachada oeste	1,20	1,40	+0,90	1
V-45	Ventana 2 hojas	Fachada oeste	1,20	1,40	+0,90	1


Nivel	Cota	Alt. libre	Destino	Estructura
Terreno natural	-0,45	—	Exterior	—
Pavimento de concreto	-1,05	—	Cemento corado 8,70 x 0,25	Cemento 3,8 x 25 N.P.M.
N.P.T. planta baja	+0,00	2,80 m	Dormitorios - SS.HH. - escalera	Losa aligerada 4x0,30 m
N.P.T. planta alta	+1,25	2,80 m	Dormitorios - estudio	Losa aligerada 4x0,30 m
N.P.T. azotea	+0,20	—	Cubierta transitable	Pendiente 2 %
Remate de parapeto	+1,55	0,90 m	Parapeto pintado	Alcantara de concreto

AMOBILIAMIENTO TIPO — DORMITORIO DOBLE (11,36 m²)

- 2 camas de 1,60 x 2,00 m, 2 escritorios de 1,20 x 0,60 m y 1 ropero.
- SS.HH. por nivel: 3 inodoros, 3 lavabos, 2 duchas y 1 urinario.
- Alfom: 18 camas por nivel - 32 camas en total.

NOTAS

- Paseo central de 1,70 m libre (anchura mínima de circulación).
- Puertas de dormitorio 0,90 m y de SS.HH. 0,80 m.
- Dormitorios con ventilación cruzada (fachadas opuestas).

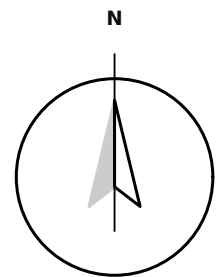

JMDSI · INGENIERIA Y ARQUITECTURA				LÁMINA A-01
Plano de proyecto — Bloque Dormitorios				E E 1:50
1 de 1		Emisión inicial		
UBICACIÓN DEL PROYECTO		FECHA		
Campus JMDSI — predio 100,00 x 100,00 m		2026-10-04		
PROYECTO		ÁREA DE PROYECTOS		
BLOQUE DORMITORIOS — 2 NIVELES (PLANTA BAJA Y ALTA)		JMDSI · Área de Proyectos		
CÓDIGO DEL PLAN		ESCALA		
PLANTA BAJA — planta de arquitectura amobliada, ejes y cotes		E 1:50	A-01	