


CORTE A-A · TRANSVERSAL

E 1:50

Cruje de 9.60 m — niveles ±0.00 — +3.25 — +6.20

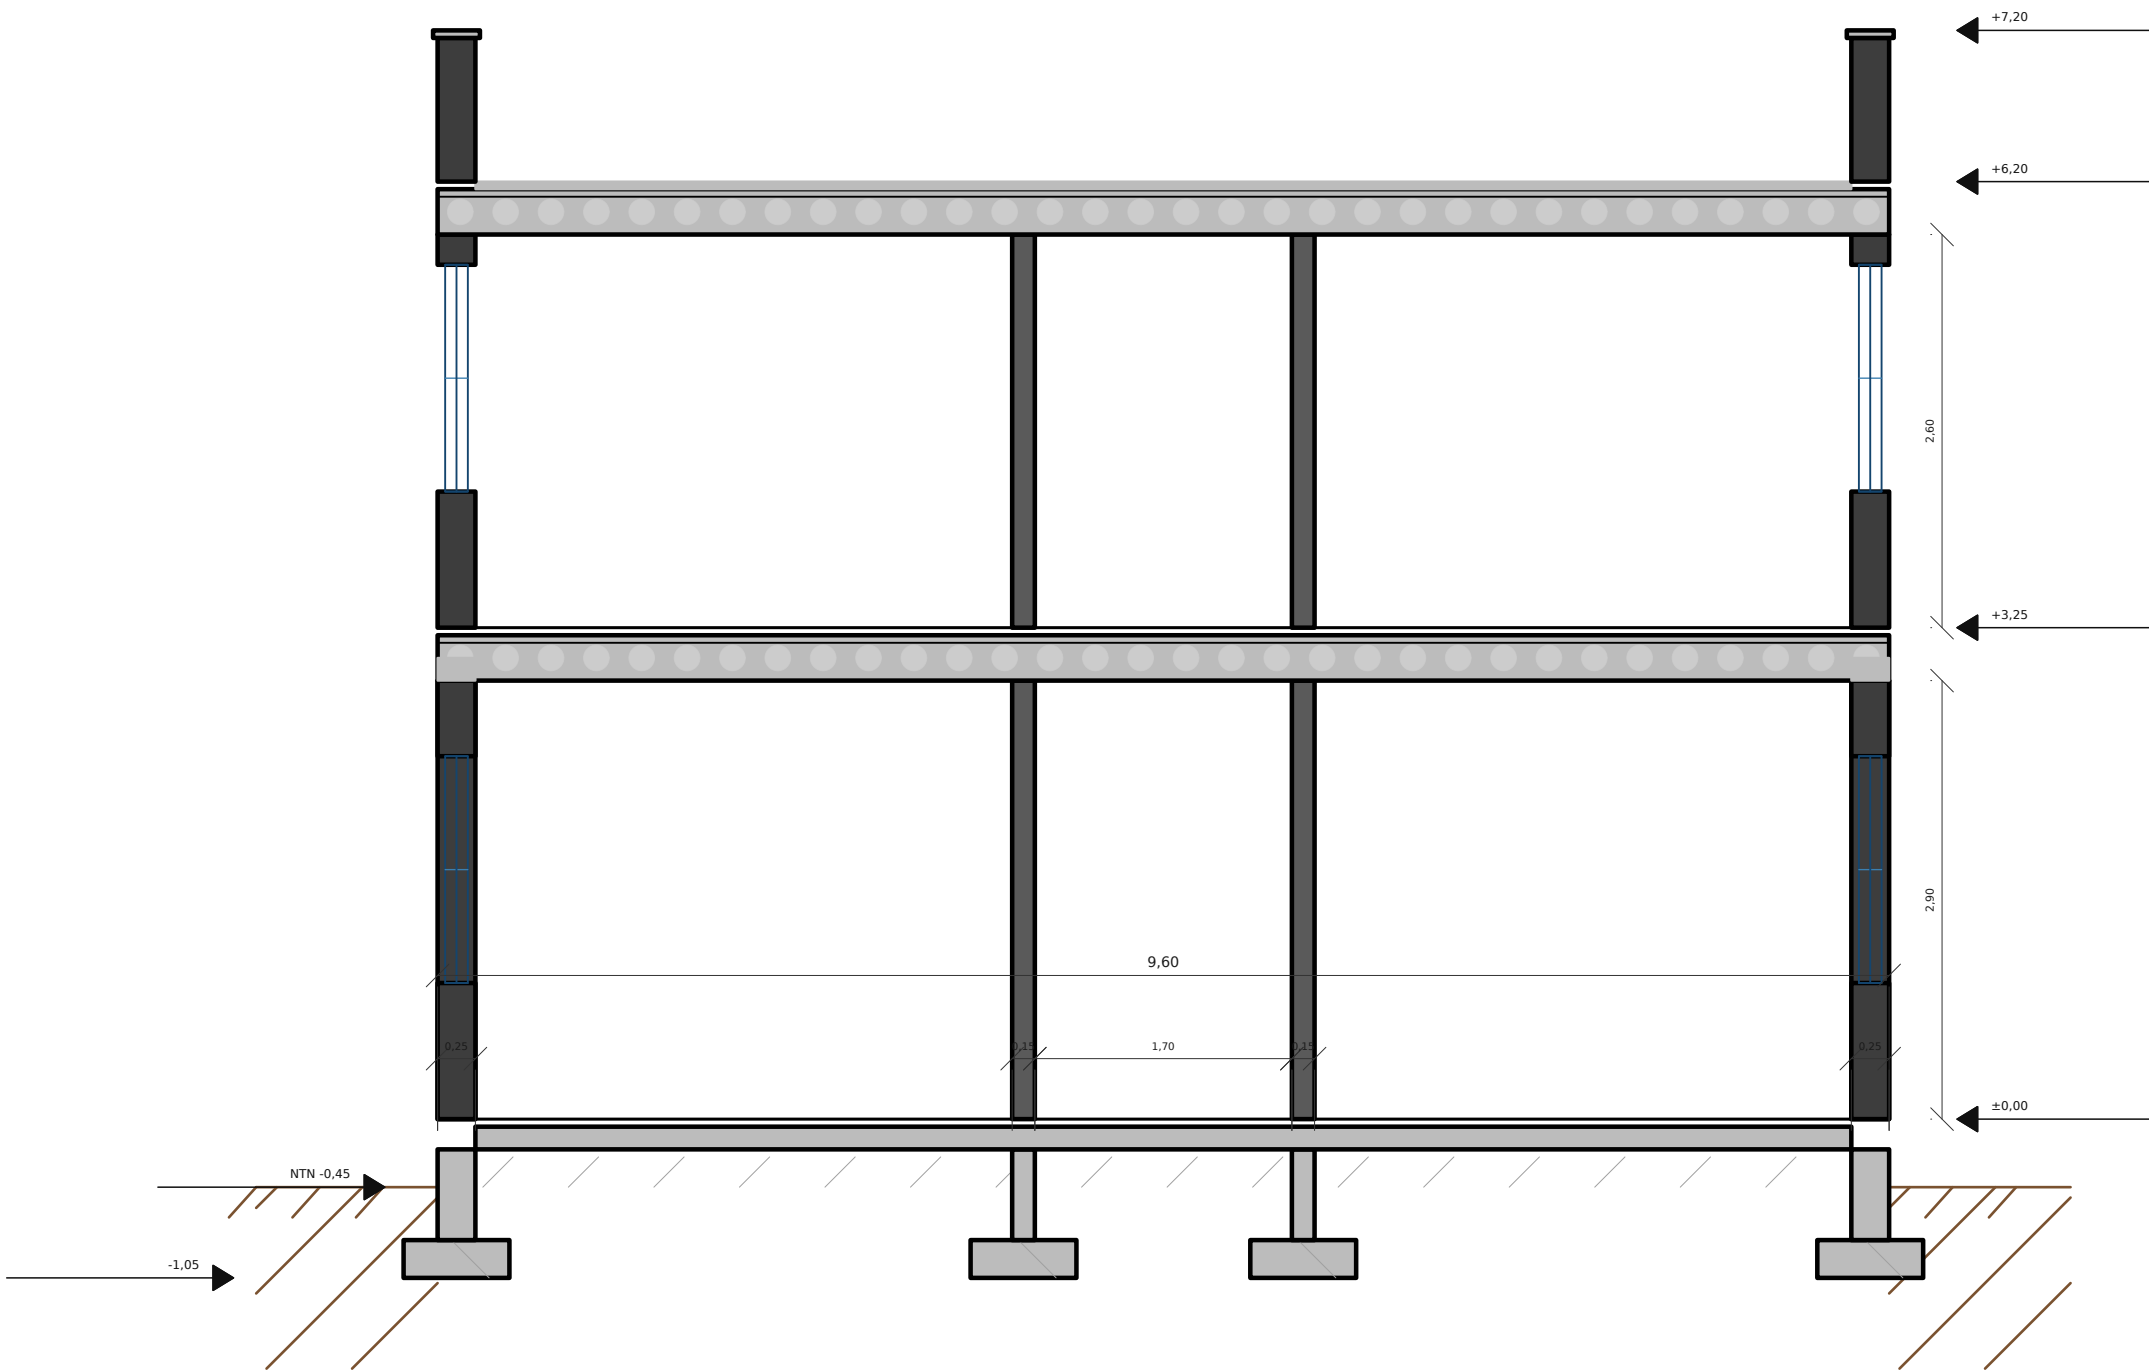

Nivel	Cota	Alt. libre	Destino	Estructura
Terreno natural	-0.45	—	Exterior	—
Fondo de cimiento	-1.05	—	Cimiento corrido 0.70 x 0.25	Concreto L-8 x 25 % F.M.
N.P.T. planta baja	+0.00	2.80 m	Dormitorios, SS.HH., escalera	Losa aligerada h=0.30 m
N.P.T. planta alta	+3.25	2.80 m	Dormitorios, estudio	Losa aligerada h=0.30 m
N.P.T. acotada	+6.20	—	Cubierta inaccesible	Pendiente 2 %
Remate de parapeto	+7.15	0.95 m	Parapeto perimetral	Alardilla de concreto

NOTAS DE CORTE

- Losa aligerada h = 0.30 m en ambos ejes.
- Vigas perfiladas de borde en las fachadas norte y sur.
- Albañilería confinada con columnas de amarre en los ejes.
- Concreto estructural Fc = 210 kg/cm², acero fy = 4 200 kg/cm².



CORTE B-B · LONGITUDINAL

E 1:50


Tramo 2 — Sobre Alameda

Longitud de 24.00 m — planta baja y planta alta

DETALLE 1 · CIMIENTO CORRIDO

E 1:20


Concreto, albañilería y sillería

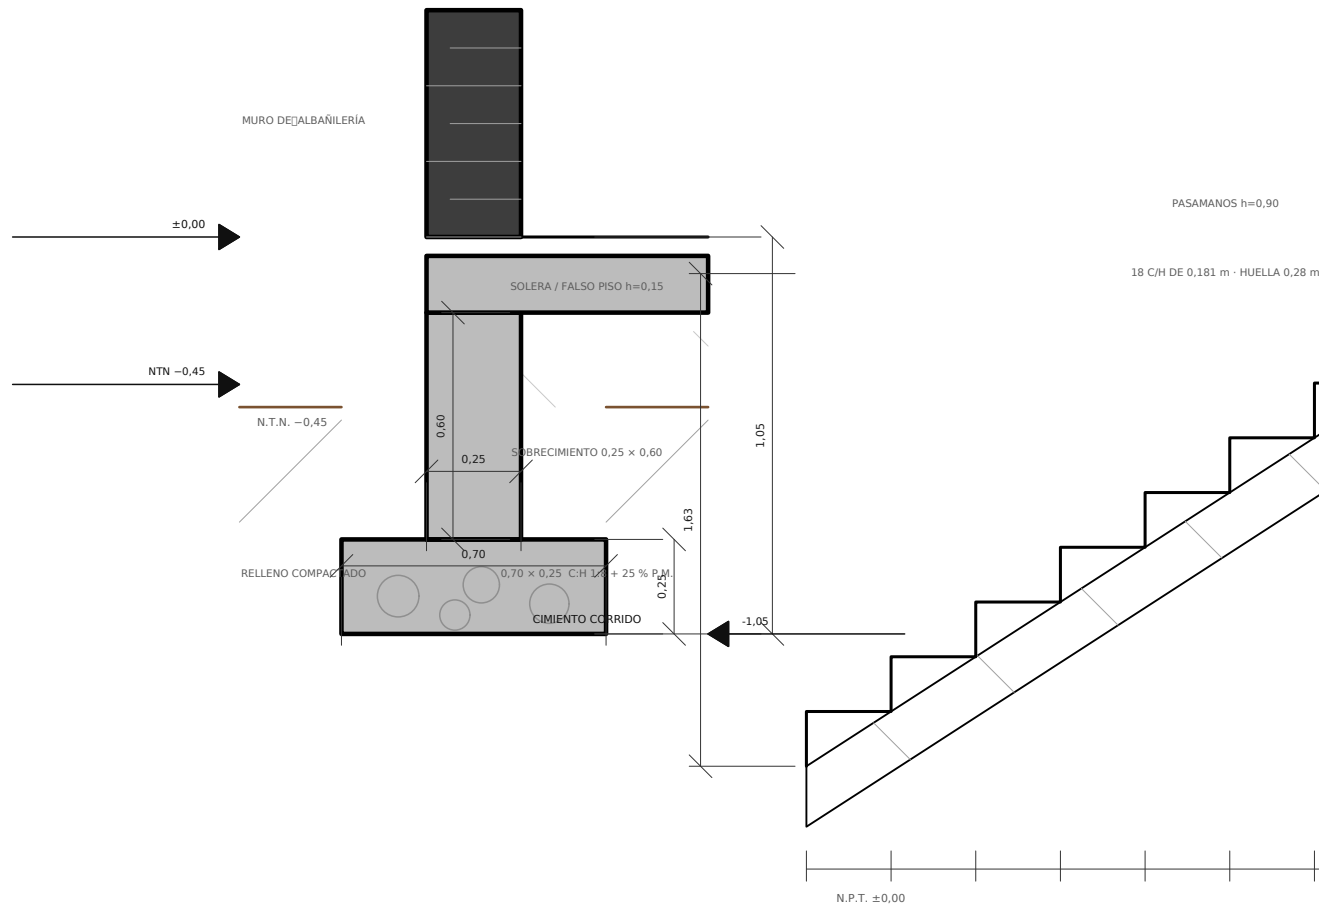

DETALLE 2 · ALERO Y PARAPETO

E 1:20


Encuentro de losa del acotado con parapeto

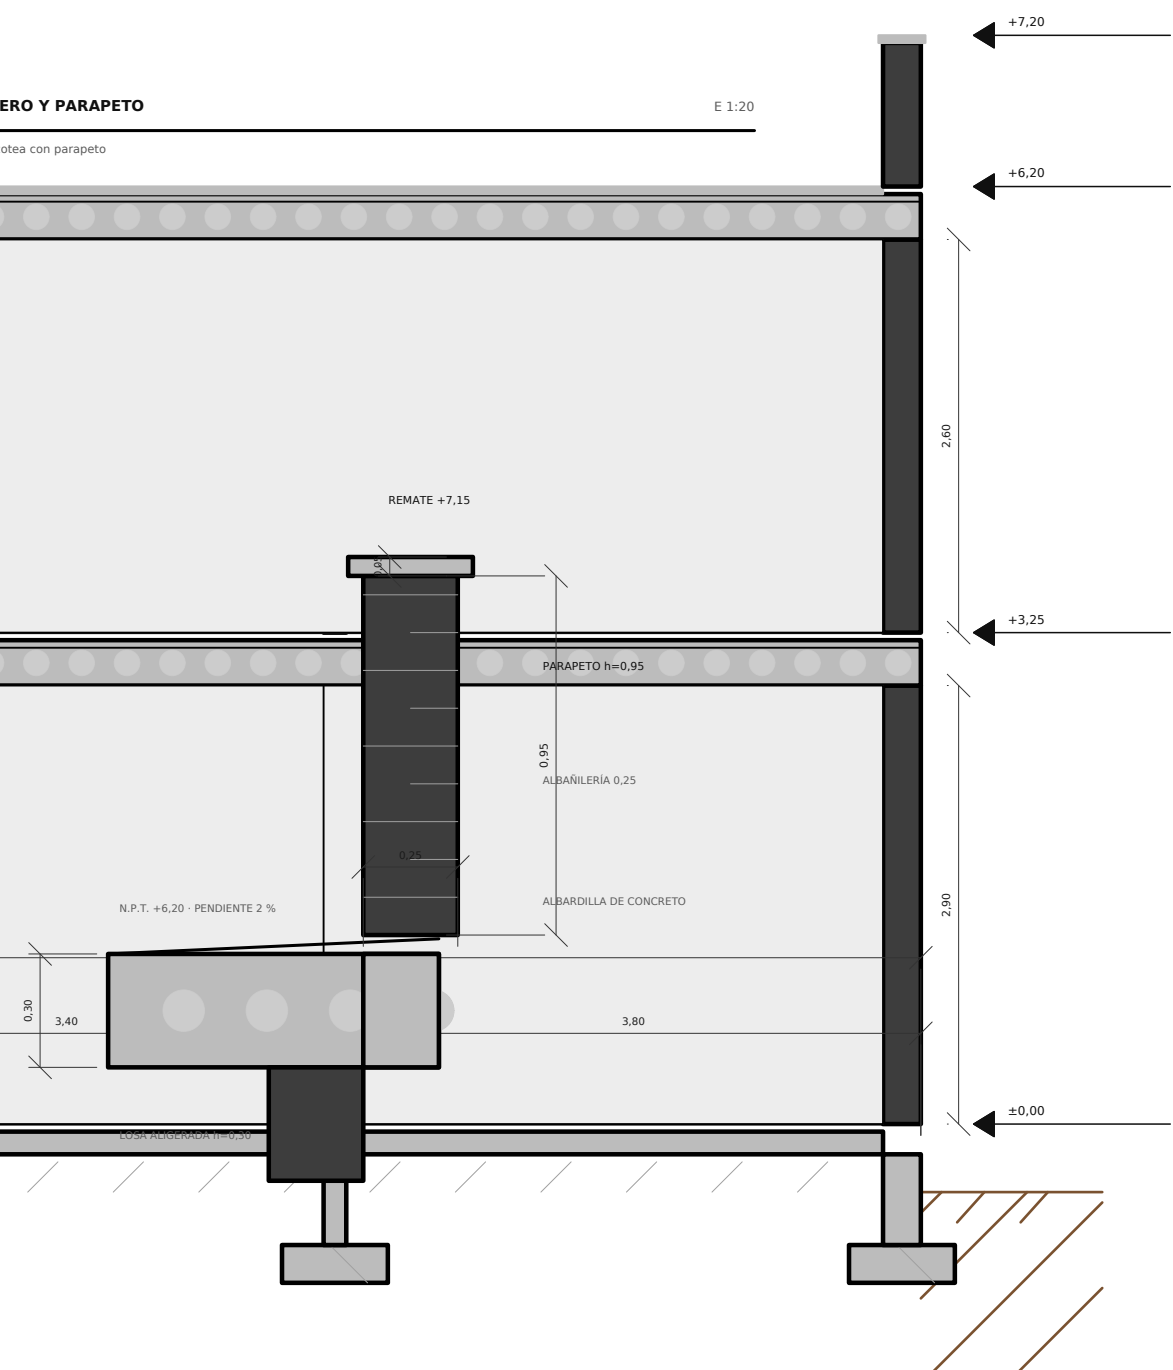

DETALLE 3 · ESCALERA

E 1:25

2 tramos — 18 CH de 0.181 m — huella 0.28 m

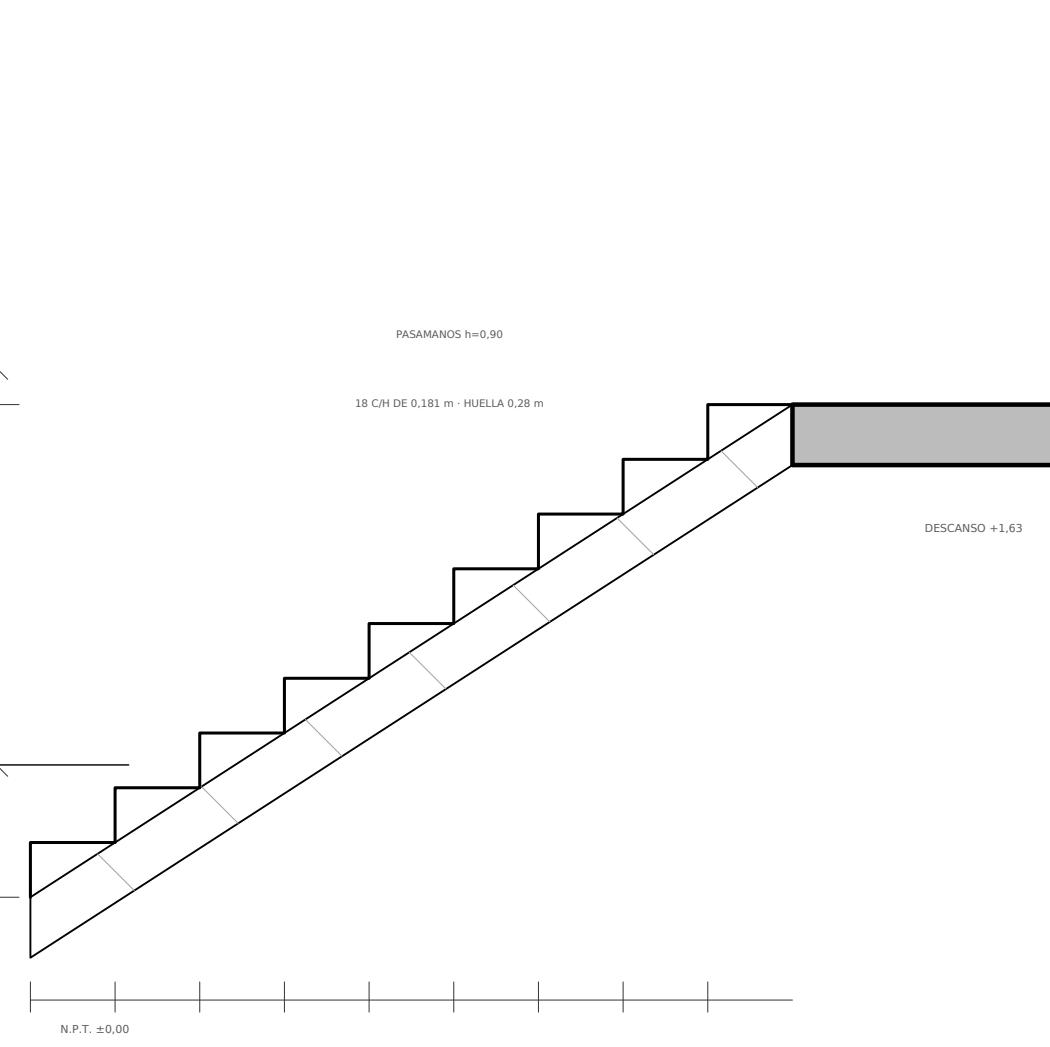

JMDSI · INGENIERIA Y ARQUITECTURA

LÁMINA A-03

Planos de proyecto — Bloque Dormitorios

E E 1:50 / 1:20 / 1:25

1 de 1

Emisión inicial

Ubicación del proyecto

Fecha

Campus JMDSI — predio 100.00 x 100.00 m

2026-10-04

BLOQUE DORMITORIOS — 2 NIVELES (PLANTA BAJA Y ALTA)

JMDSI · Área de Proyectos

Cortes A-A y B-B (planta baja y alta) + detalles constructivos

E 1:50 / 1:20 A-03