



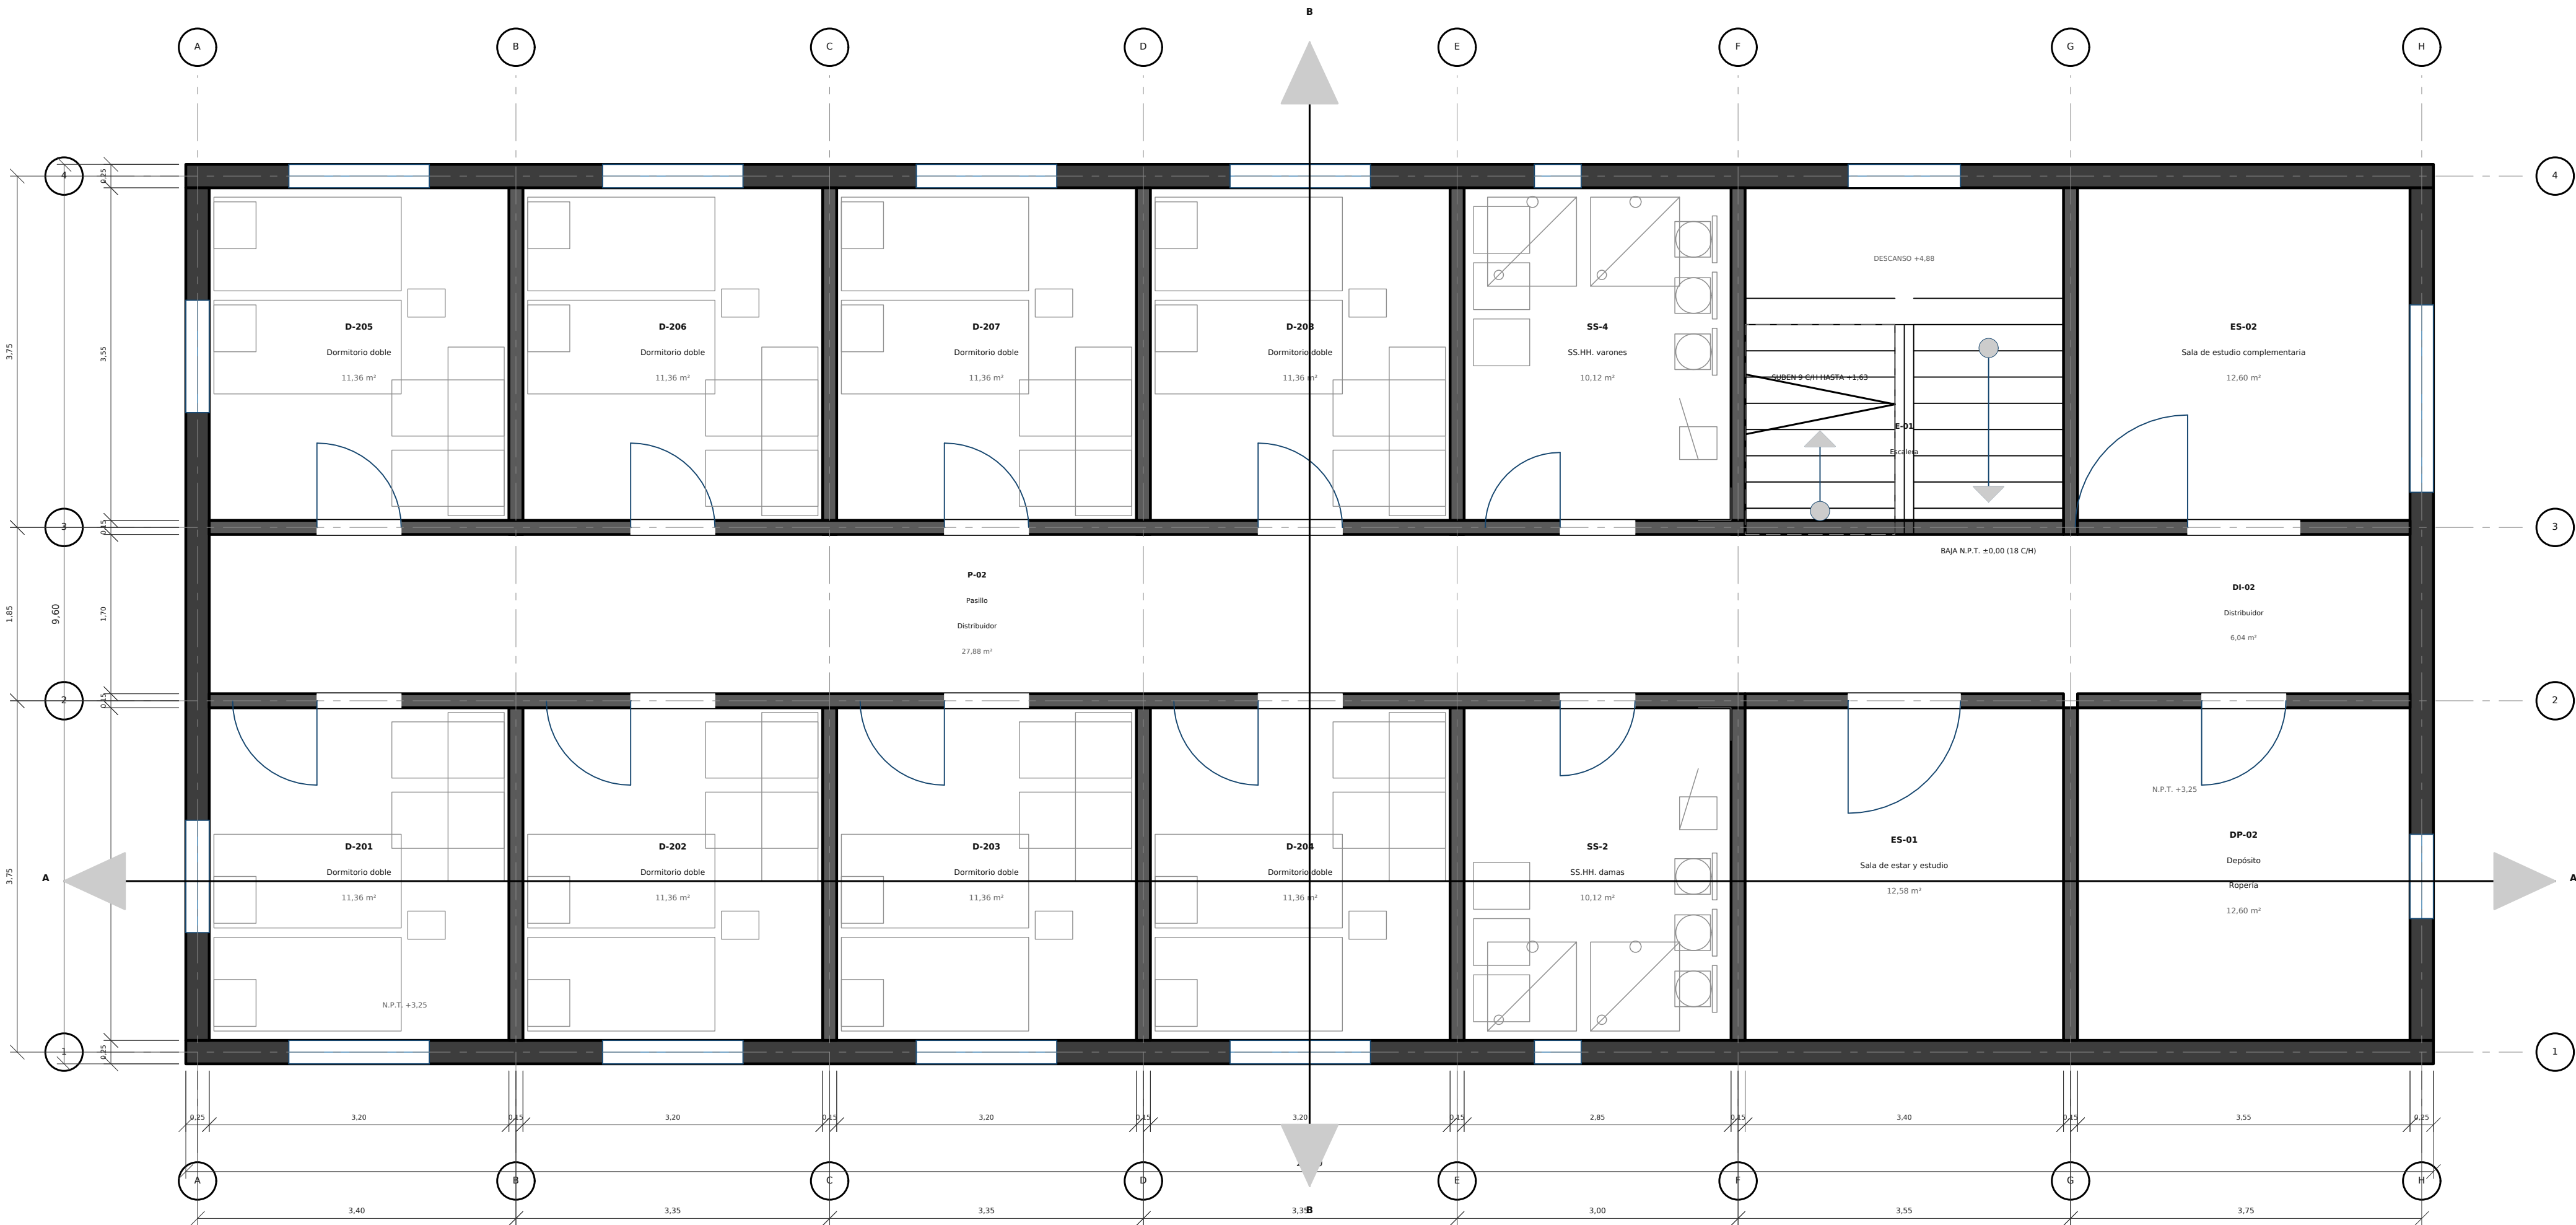

PLANTA ALTA · N.P.T. +3,25
Escala 1:50 - celda en metros - modulator tipo

SITUACIÓN · BLOQUE DORMITORIOS (D)

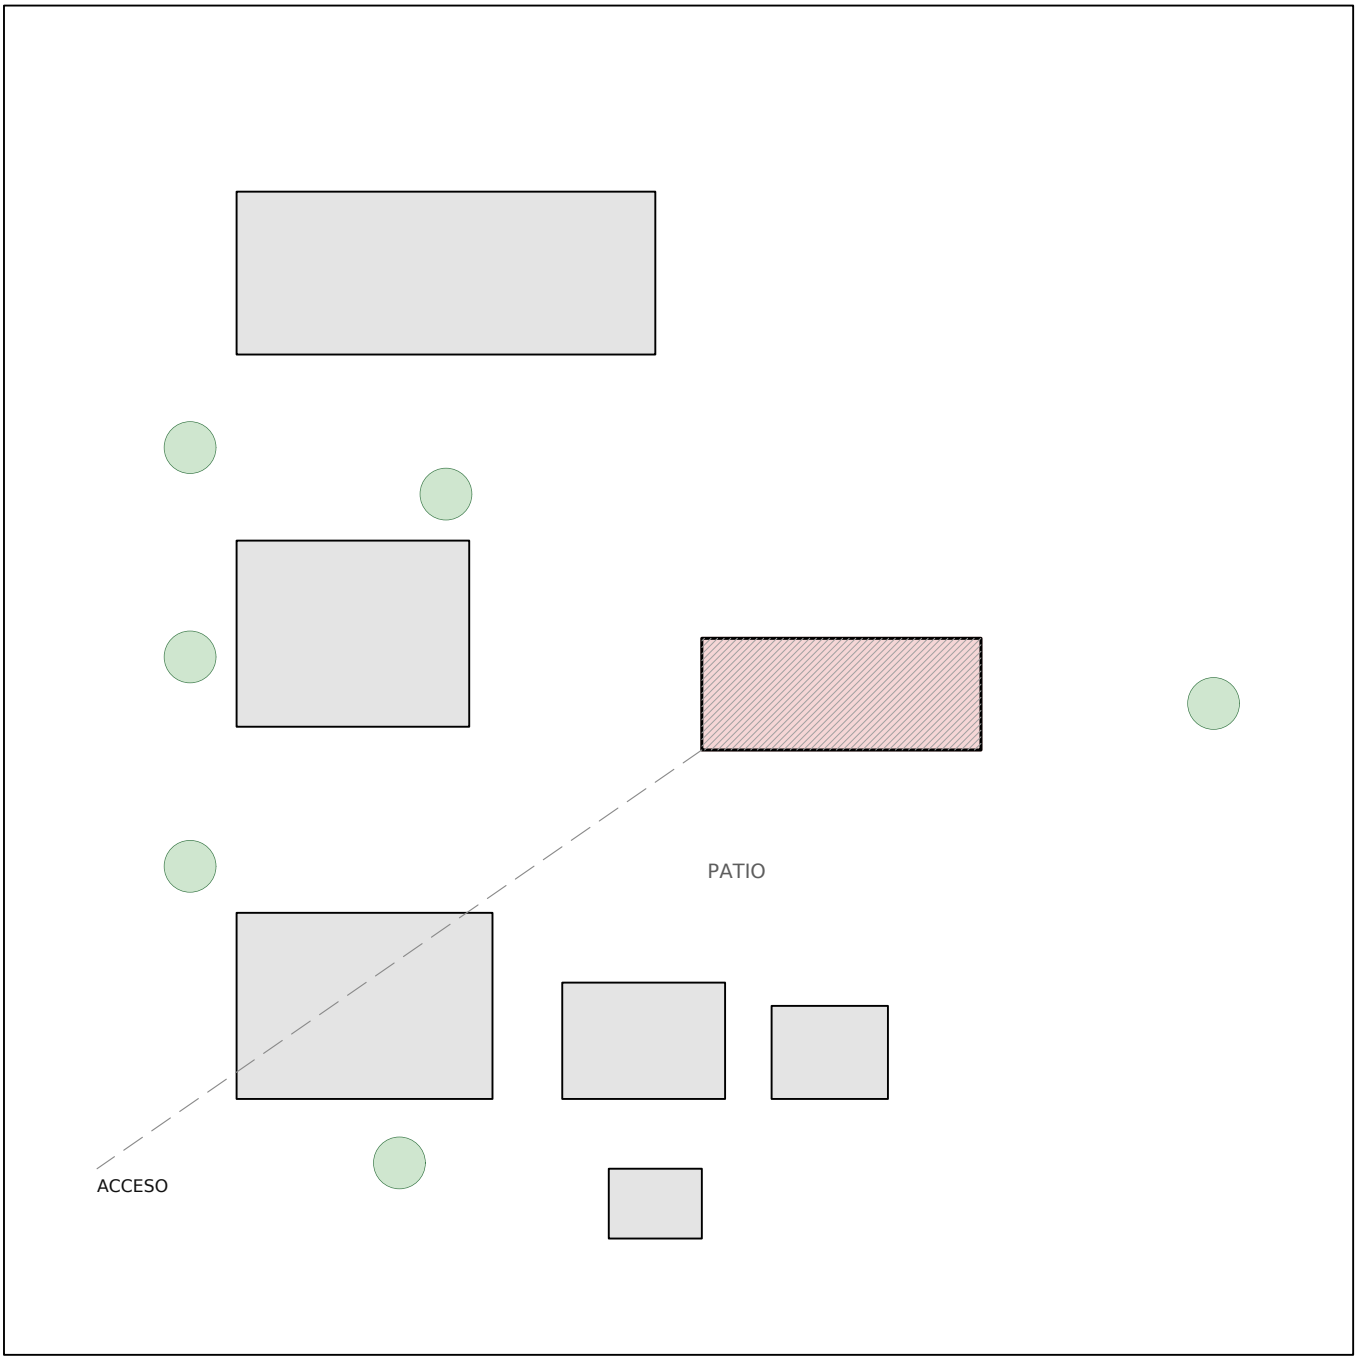

Escala 1:500 - predio de 100.00 x 100.00 m

Nivel	Cód.	Recinto	Área (m²)
P. ALTA	D-201	Dormitorio doble	11,36
P. ALTA	D-202	Dormitorio doble	11,36
P. ALTA	D-203	Dormitorio doble	11,36
P. ALTA	D-204	Dormitorio doble	11,36
P. ALTA	D-205	Dormitorio doble	11,36
P. ALTA	D-206	Dormitorio doble	11,36
P. ALTA	D-207	Dormitorio doble	11,36
P. ALTA	D-208	Dormitorio doble	11,36
P. ALTA	SS-2	SS.HH. damas	10,12
P. ALTA	SS-4	SS.HH. varones	10,12
P. ALTA	P-02	Paseo	27,88
P. ALTA	ES-01	Sala de estar y estudio	12,60
P. ALTA	ES-02	Sala de estudio complementaria	12,60
P. ALTA	DP-02	Deposito / Reparto	12,60
P. ALTA	DI-02	Distribuidor	6,04

Eje	X (m)	Entre ejes	Eje	Y (m)	Entre ejes
A	0,12	—	1	0,12	—
B	3,52	3,40	2	3,68	3,75
C	6,88	3,35	3	5,72	1,85
D	10,22	3,35	4	9,47	3,75
E	13,57	3,35			
F	16,92	3,00			
G	20,12	3,55			
H	23,88	3,75			

Nº	Tipo	Ubicación	Ancho	Alto	Abrir	Cont.
V-105	Ventana 2 hojas	Fachada norte	1,50	1,50	+4,15	1
V-106	Ventana 2 hojas	Fachada norte	1,50	1,50	+4,15	1
V-107	Ventana 2 hojas	Fachada norte	1,50	1,50	+4,15	1
V-108	Ventana 2 hojas	Fachada norte	1,50	1,50	+4,15	1
V-205	Ventana 2 hojas	Fachada sur	1,50	1,50	+4,15	1
V-206	Ventana 2 hojas	Fachada sur	1,50	1,50	+4,15	1
V-207	Ventana 2 hojas	Fachada sur	1,50	1,50	+4,15	1
V-208	Ventana 2 hojas	Fachada sur	1,50	1,50	+4,15	1
V-32	Ventana alta	Fachada norte	0,50	0,80	+4,95	1
V-34	Ventana alta	Fachada sur	0,50	0,80	+4,95	1
V-42	Ventana	Fachada norte	1,20	0,85	+5,80	1
V-47	Ventana	Fachada este	2,00	1,70	+6,80	1
V-48	Ventana	Fachada este	0,80	1,00	+6,75	1
V-49	Ventana 2 hojas	Fachada este	1,20	1,40	+6,15	1
V-50	Ventana 2 hojas	Fachada este	1,20	1,40	+6,15	1


Nivel	Cota	Alt. libre	Destino	Estructura
Terreno natural	-0,45	—	Exterior	—
Pavimento exterior	-1,05	—	Cemento corado 8,70 x 0,25	Cemento 1:8 = 25 N.P.M.
N.P.T. planta baja	+0,00	2,80 m	Dormitorios - SS.HH. - escalera	Losa aligerada 4x0,30 m
N.P.T. planta alta	+3,25	2,80 m	Dormitorios - estudio	Losa aligerada 4x0,30 m
N.P.T. azotea	+5,20	—	Cubierta (accesos)	Pendiente 2 %
Remate de parapeto	+7,15	0,90 m	Parapeto perimetral	Alcantara de concreto

AMOBILIARIO TIPO — DORMITORIO DOBLE (11,36 m²)

- 2 camas de 1,60 x 2,00 m, 2 escritorios de 1,20 x 0,60 m y 1 ropero.
- SS.HH. por nivel: 3 inodoros, 3 lavabos, 2 duchas y 1 urinario.
- Alfombras: 18 camas por nivel - 32 camas en total.

NOTAS

- Paseo central de 1,70 m libre (anchura mínima de circulación).
- Puertas de dormitorio 0,80 m y de SS.HH. 0,80 m.
- Dormitorios con ventilación cruzada (fachadas opuestas).

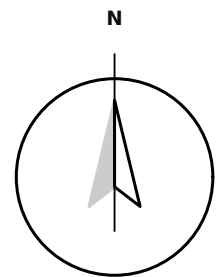

5 m

JMDSI · INGENIERÍA Y ARQUITECTURA				LÁMINA A-02	
Plano de proyecto — Bloque Dormitorios				E E 1:50	
1 de 1		Emisión inicial		FECHA	
VERIFICACIÓN DE INFORMACIÓN		2026-10-04		VERIFICACIÓN	
Campus JMDSI — predio 100.00 x 100.00 m				JMDSI · Área de Proyectos	
BLOQUE DORMITORIOS — 2 NIVELES (PLANTA BAJA Y ALTA)					
VERIFICACIÓN		Escala A		B1	
PLANTA ALTA : planta de arquitectura amoblada, ejes y cotas		E 1:50		A-02	